



FLOOR PLATE OUTLINE — FOR HAND SKETCHING

PRINT AT 100% / ACTUAL SIZE — do not 'fit to page'

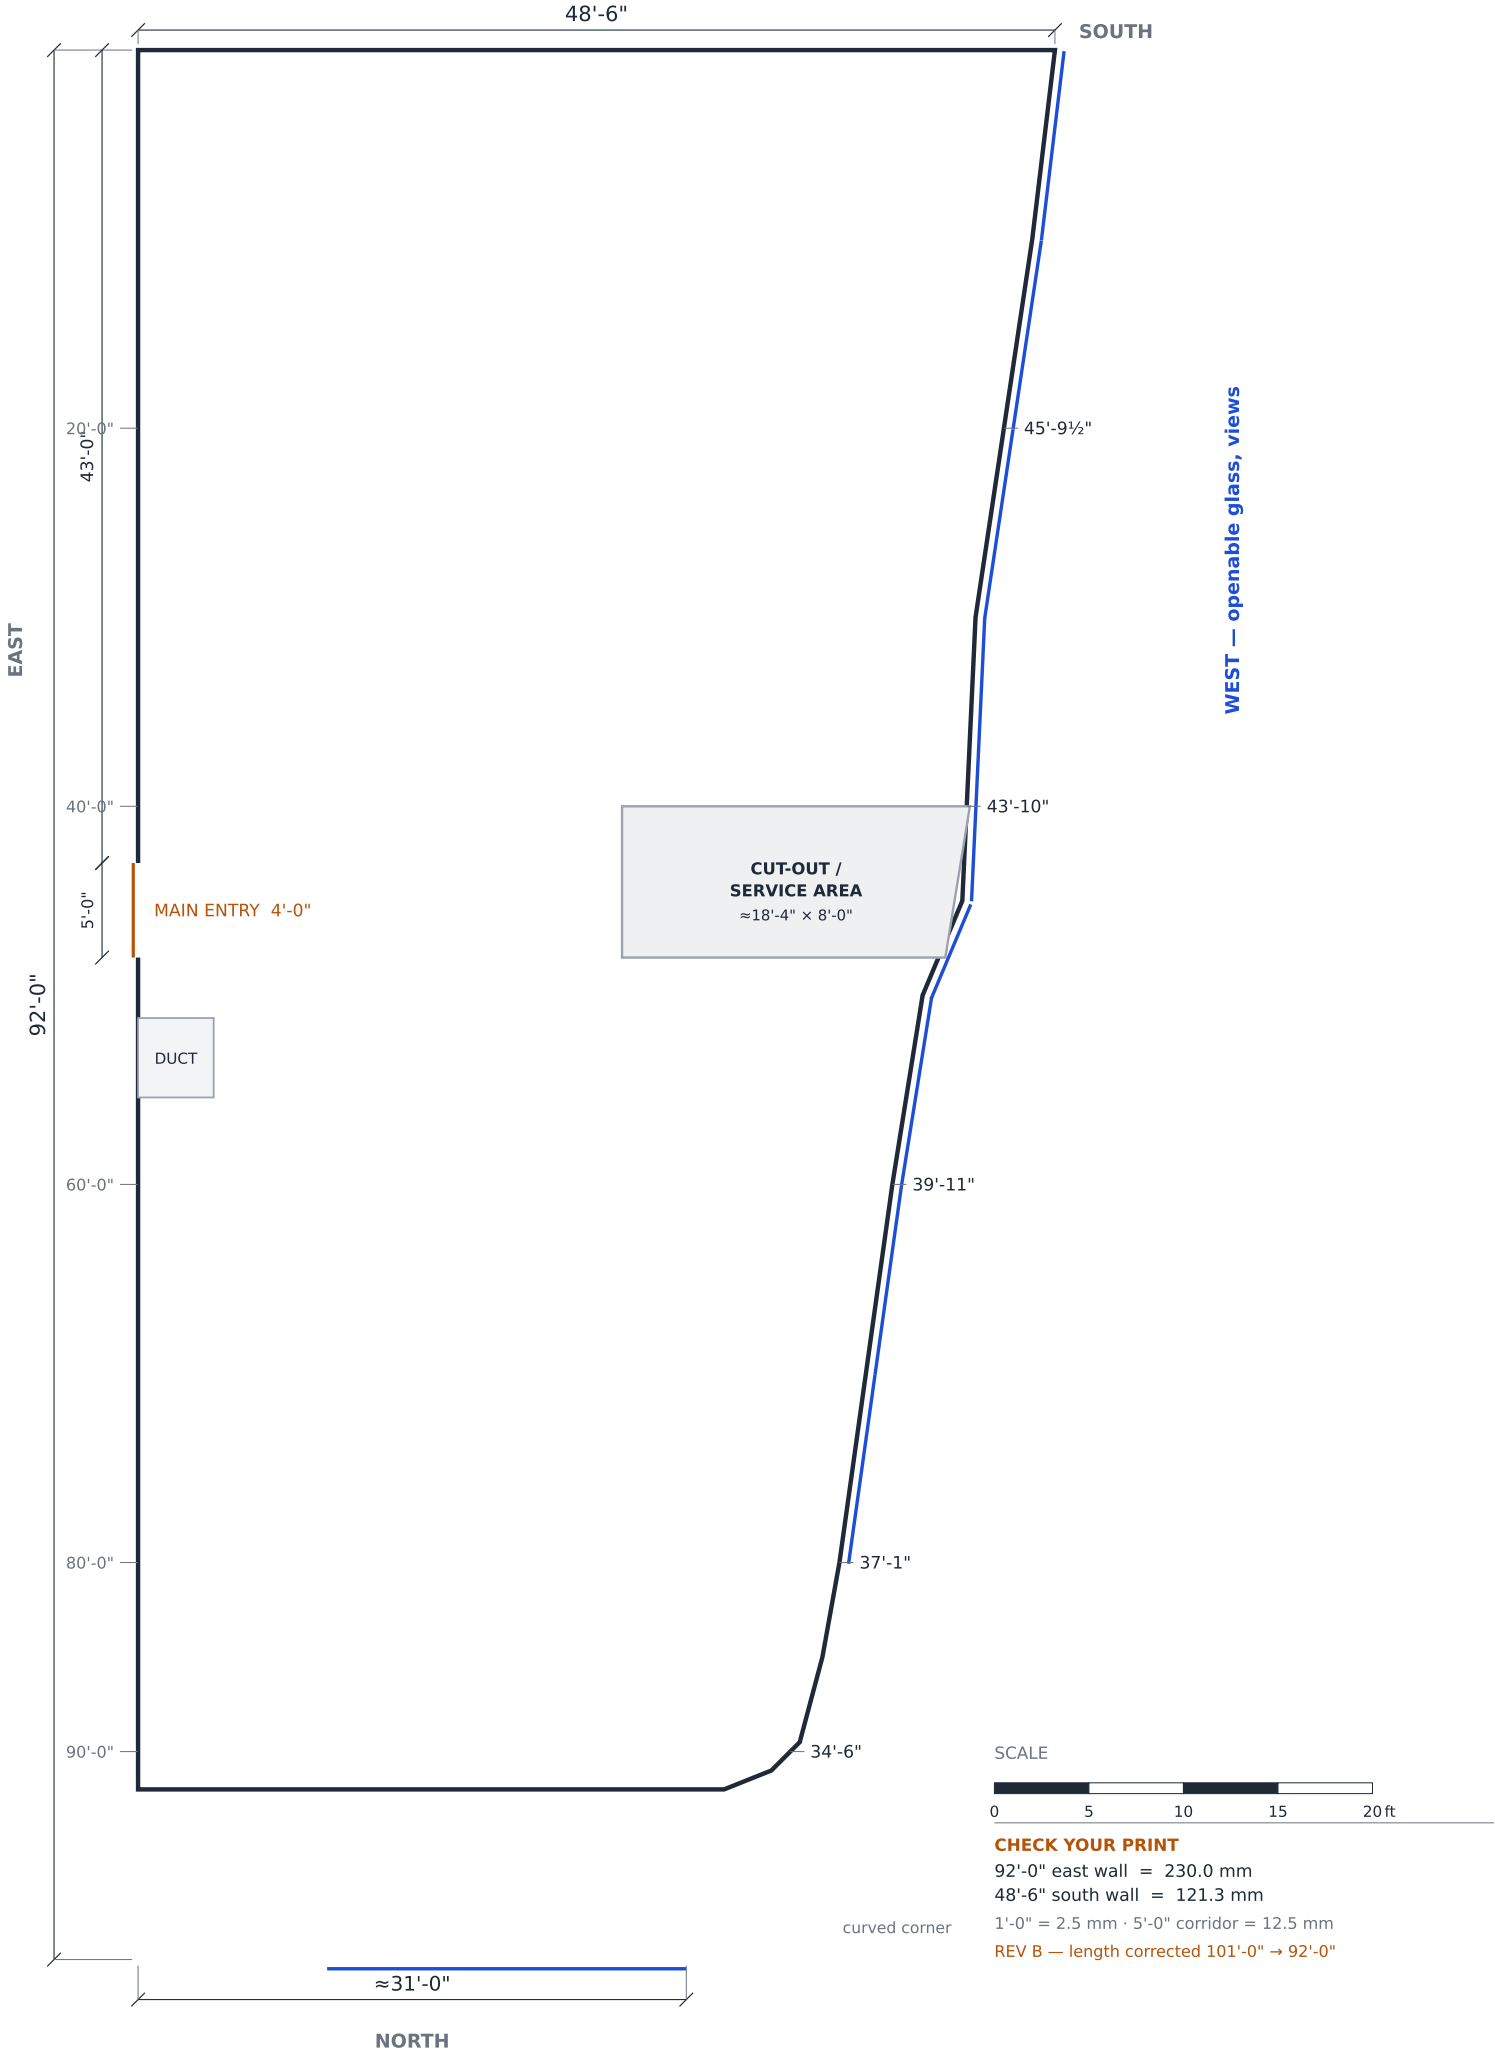

FLOOR PLATE OUTLINE — 4'-0" SKETCHING GRID

PRINT AT 100% / ACTUAL SIZE — do not 'fit to page'

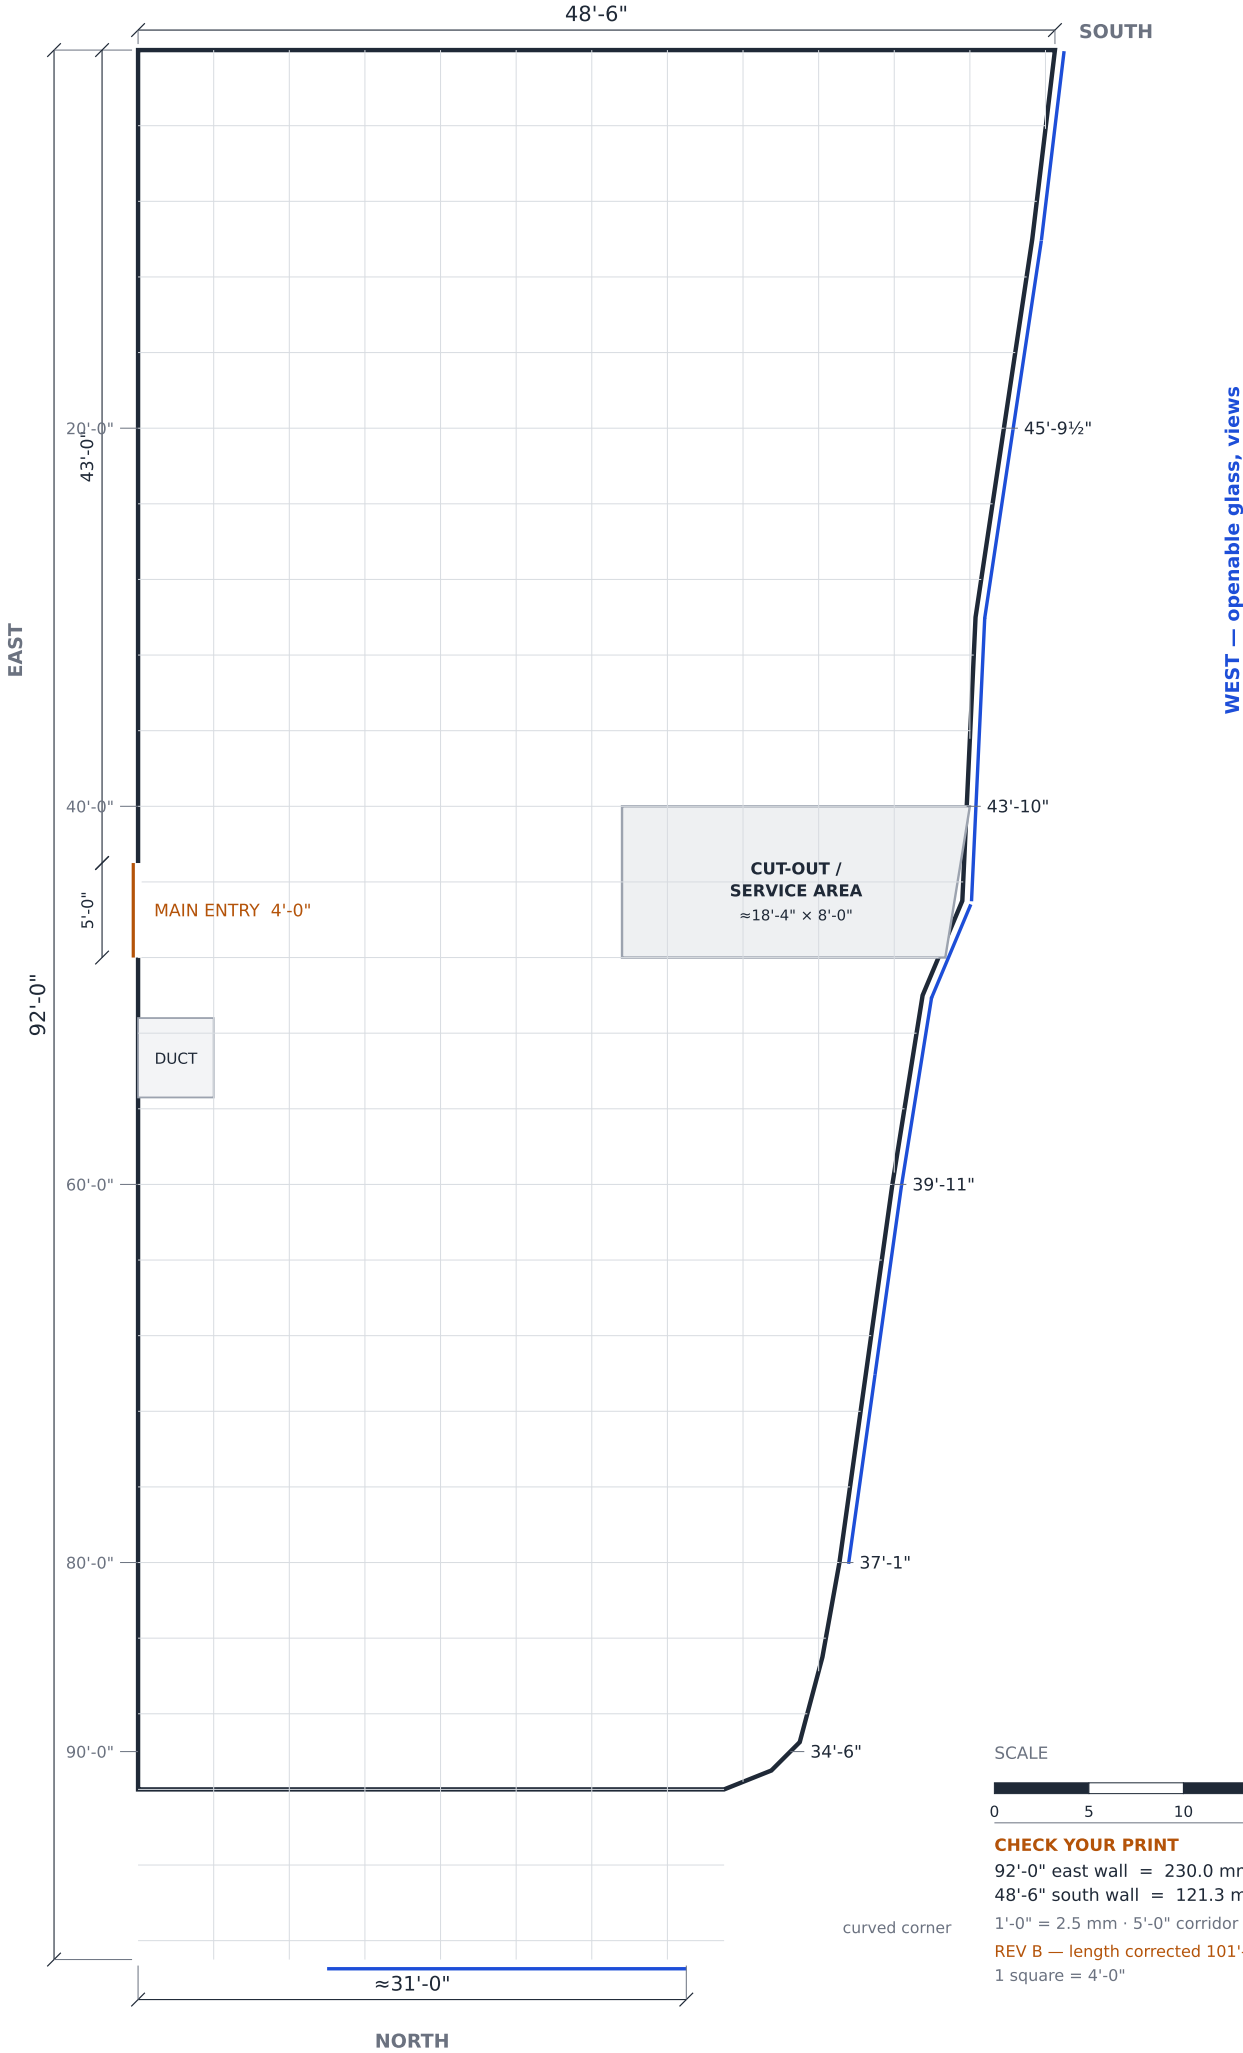

SCALE

0 5 10 15 20 ft

CHECK YOUR PRINT

92'-0" east wall = 230.0 mm

48'-6" south wall = 121.3 mm

1'-0" = 2.5 mm · 5'-0" corridor = 12.5 mm

REV B — length corrected 101'-0" → 92'-0"

1 square = 4'-0"

OVERALL ENVELOPE (REVISION B — see notes)

South wall (top of sheet)	48' -6"
East wall — straight, full length	92' -0"
North wall (short, past the curved corner)	≈ 31' -0"
Gross area inside the envelope	≈ 3,871 sq ft
Net, after deducting the cut-out	≈ 3,729 sq ft

WEST FACADE — WIDTH AT EACH STATION

at 0'-0" (south wall)	48' -6"
at 10'-0" north of the south wall	47' -3½"
at 20'-0"	45' -9½"
at 30'-0"	44' -3½"
at 45'-0" (cut-out corner — slight jog)	43' -7"
at 50'-0"	41' -6"
at 60'-0"	39' -11"
at 70'-0"	38' -6"
at 80'-0"	37' -1"
at 89'-6" (curve begins)	35' -0"
at 92'-0" (north wall)	≈ 31' -0"

FIXED CONSTRAINTS — DO NOT BUILD OVER

Main entry door, east wall, from the south corner	43' -0" to 48' -0"
Cut-out / service void — east edge, from east wall	25' -7"
Cut-out — south edge, from the south wall	40' -0"
Cut-out — size (runs west to the facade)	≈ 18' -4" × 8' -0"
Duct / shaft on the east wall (TRACED — VERIFY)	≈ 51' -2", 4' -0" × 4' -2"
Openable glass	whole west facade + north edge
Service area (outside the tenancy)	strip beyond the south wall

HANDY CONVERSIONS AT THIS SCALE

1'-0"	2.5 mm
5'-0" — minimum wheelchair corridor	12.5 mm
10'-0"	25 mm
Typical single room, 12'-0" × 9'-0"	30 × 22.5 mm
Hospital bed, 3'-3" × 6'-6"	8 × 16 mm
Operation theatre, 20'-0" × 17'-0"	50 × 42.5 mm

NOTES

- REVISION B: the envelope was re-surveyed from the architect's sheet and the length corrected from 101'-0" to 92'-0". Layouts A-D were drawn on the old, over-long plate and must be re-fitted to this outline.
- The zone marked CUT-OUT here is labelled SERVICE AREA on the builder's typical-floor plan — confirm whether it has a slab before planning it.
- Geometry is traced from a photograph of the drawing, not surveyed. Ask the builder for a DXF/PDF export to remove the remaining tracing error.
- Columns and shear walls are NOT shown — get the structural grid first.
- Keep every patient corridor at least 5'-0" clear (12.5 mm on this print).