


FLOOR PLATE OUTLINE — FOR HAND SKETCHING

PRINT AT 100% / ACTUAL SIZE — do not 'fit to page'

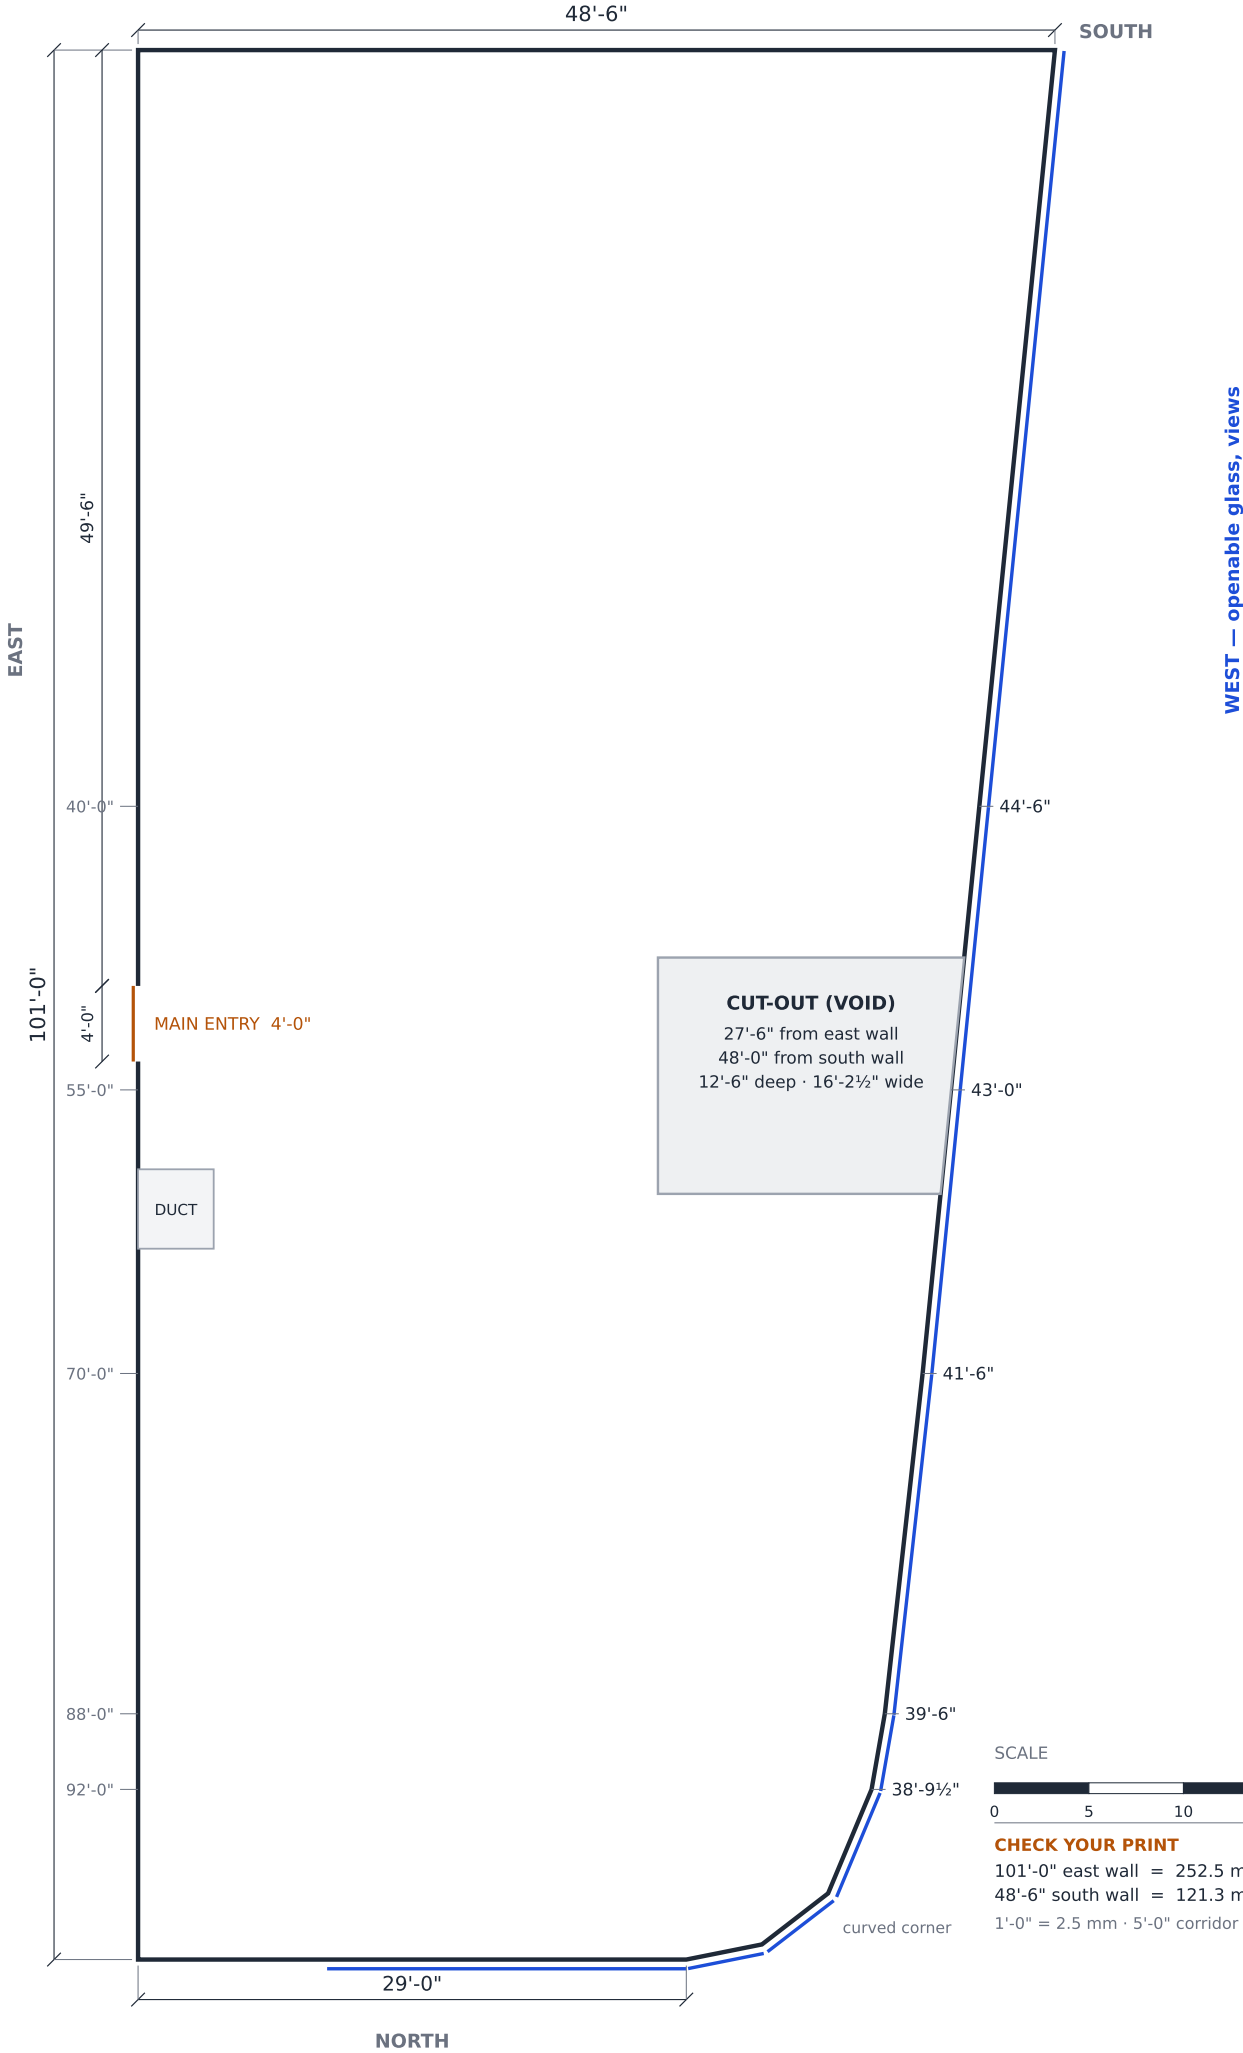

SCALE

0 5 10 15 20 ft

CHECK YOUR PRINT


101'-0" east wall = 252.5 mm

48'-6" south wall = 121.3 mm

1'-0" = 2.5 mm · 5'-0" corridor = 12.5 mm

FLOOR PLATE OUTLINE — 4'-0" SKETCHING GRID

PRINT AT 100% / ACTUAL SIZE — do not 'fit to page'

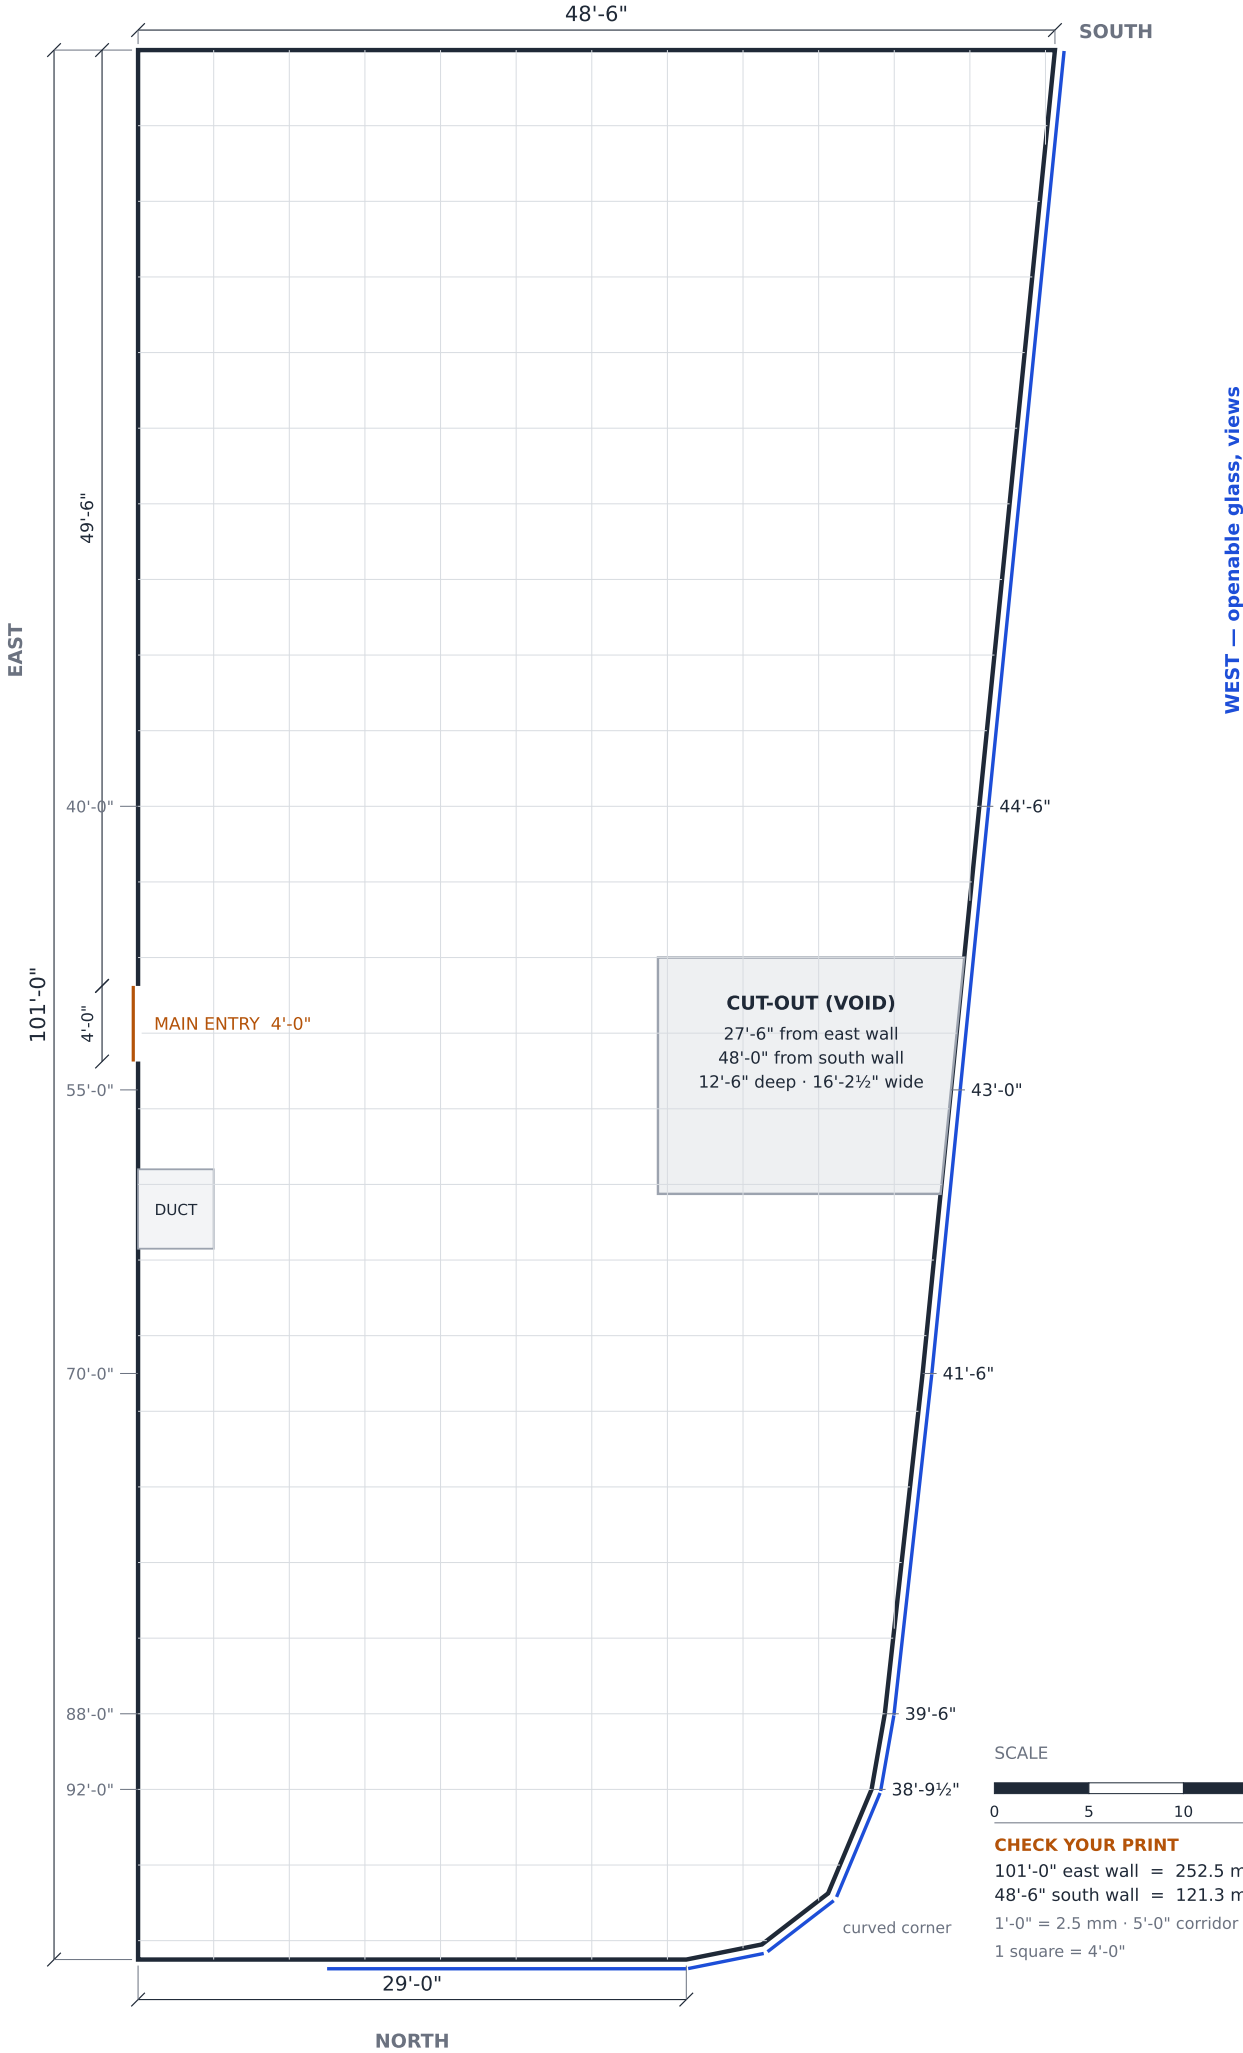

OVERALL ENVELOPE

South wall (top of sheet)	48' -6"
East wall — straight, full length	101' -0"
North wall (short, at the curved end)	29' -0"
Carpet area inside the envelope, less the cut-out	≈ 4,164 sq ft

WEST FACADE — WIDTH AT EACH STATION

at 0'-0" (south wall)	48' -6"
at 40'-0" north of the south wall	44' -6"
at 55'-0"	43' -0"
at 70'-0"	41' -6"
at 88'-0"	39' -6"
at 92'-0"	38' -9½"
at 97'-6" (curve begins)	36' -6"
at 100'-2"	33' -0"
at 101'-0" (north wall)	29' -0"

FIXED CONSTRAINTS — DO NOT BUILD OVER

Main entry door, east wall, from the south corner	49' -6" to 53' -6"
Cut-out (void) — east edge, from the east wall	27' -6"
Cut-out — south edge, from the south wall	48' -0"
Cut-out — size (runs west to the facade)	16' -2½" × 12' -6"
Duct / shaft on the east wall (TRACED — VERIFY)	≈ 59' -2", 4' -0" × 4' -2"
Openable glass	whole west facade + north edge
Service area (outside the tenancy)	beyond the south wall

HANDY CONVERSIONS AT THIS SCALE

1'-0"	2.5 mm
5'-0" — minimum wheelchair corridor	12.5 mm
10'-0"	25 mm
Typical single room, 12'-0" × 9'-0"	30 × 22.5 mm
Hospital bed, 3'-3" × 6'-6"	8 × 16 mm
Operation theatre, 20'-0" × 17'-0"	50 × 42.5 mm

NOTES

- Geometry is traced from the dimensioned floor-plan drawing, not surveyed.
- Columns and shear walls are NOT shown — get the structural grid from the DWG before you commit partitions.
- The north-west corner is curved; it is drawn here as short straight runs.
- Keep every patient corridor at least 5'-0" clear (12.5 mm on this print).